



CONCEPT, NOT FOR FABRICATION


REV	DESCRIPTION	DATE	BY
P1	Concept sheet	2026-09-25	AC

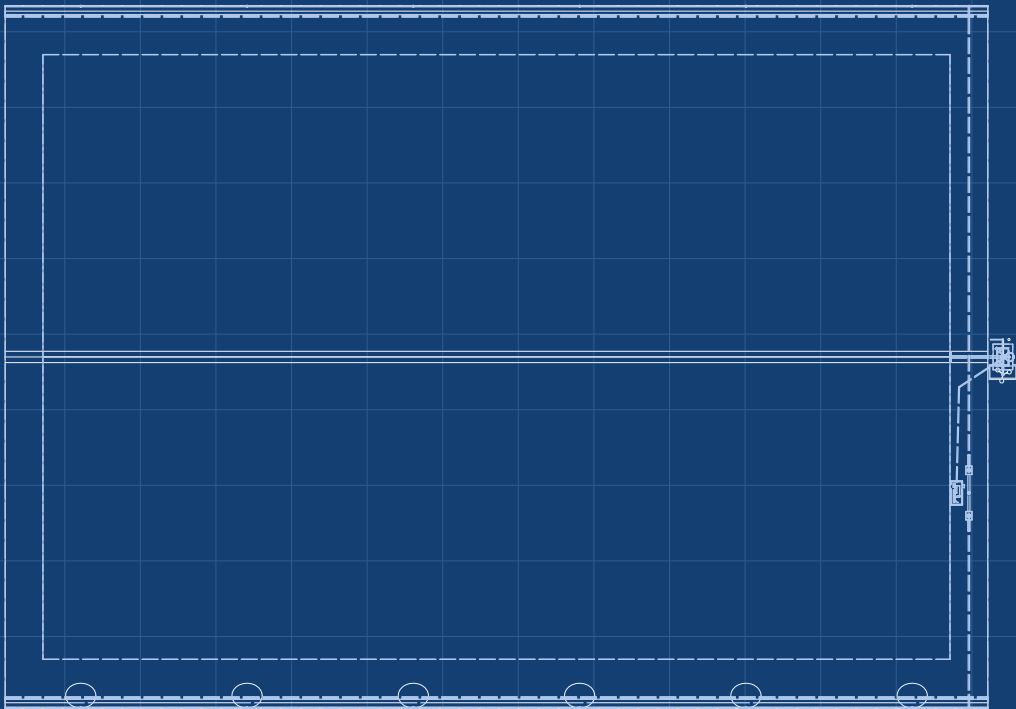


TOP VIEW
Scale 1:100

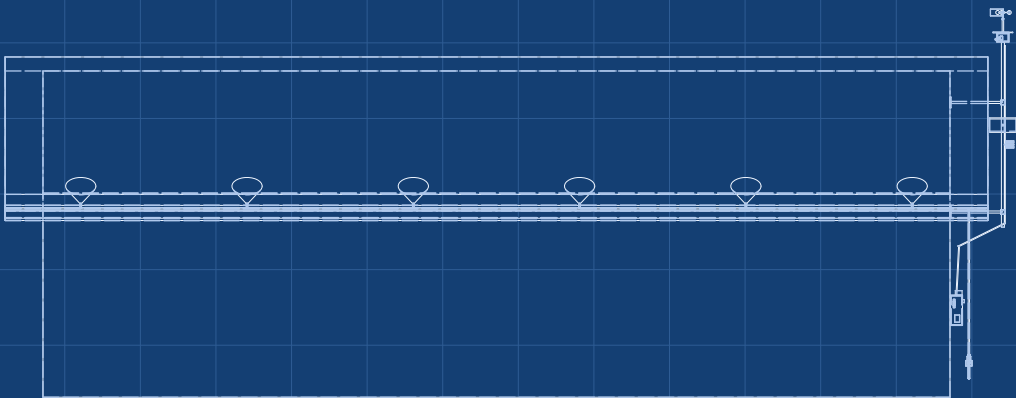

FRONT VIEW
Scale 1:100

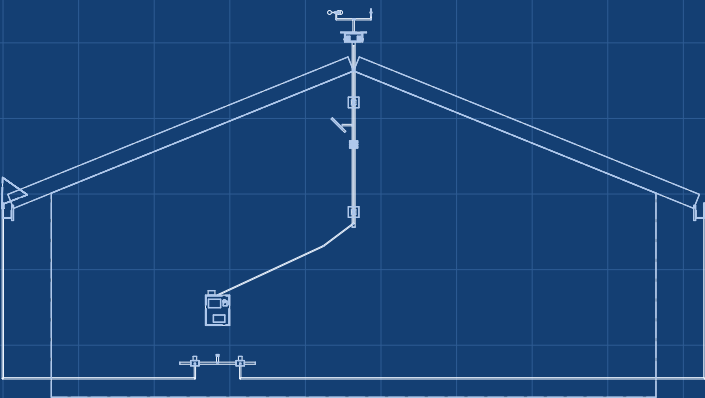

RIGHT VIEW
Scale 1:100

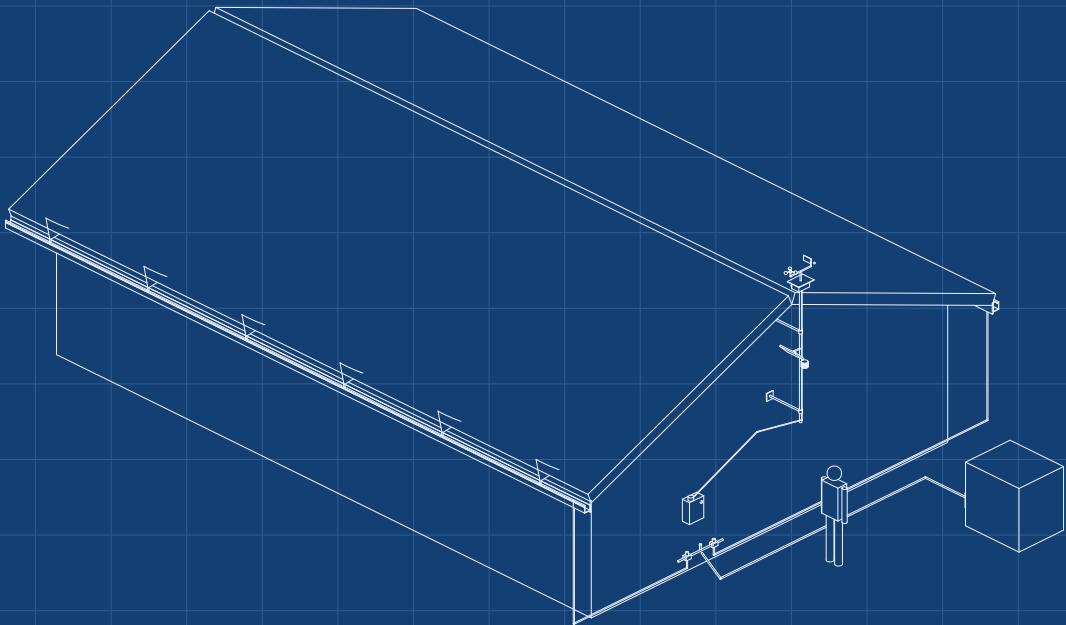

ISOMETRIC VIEW
Not to scale; figure is a 1.75 m person

KEY FIGURES

- Two 32 x 24 px thermal arrays watch both roof planes and gutters
- Arms on wind and humidity; sprays on hot spots (proposed logic)
- Two zones alternate: 4 L/min steady draw (estimate)
- About 960 L per 4 h ember event (estimate)
- 72 h armed plus 4 h spraying on a 77 Wh battery (estimate)
- Kit parts about \$420 against a \$300 budget (indicative)

EMBERGUARD

Ember watch mast and eave spray concept

DRAWING NO. EGD-DWG-010			REV P1	SHEET 1 of 1	SIZE ANSI B
SCALE 1:100	UNITS mm	PROJECTION 	DATE 2026-09-25	DRAWN Amish Chadha	

MATERIAL / NOTES
Massing model for concept communication