



CONCEPT, NOT FOR FABRICATION

EmberGuard · github.com/BoujeeEnjinia1701/emberguard

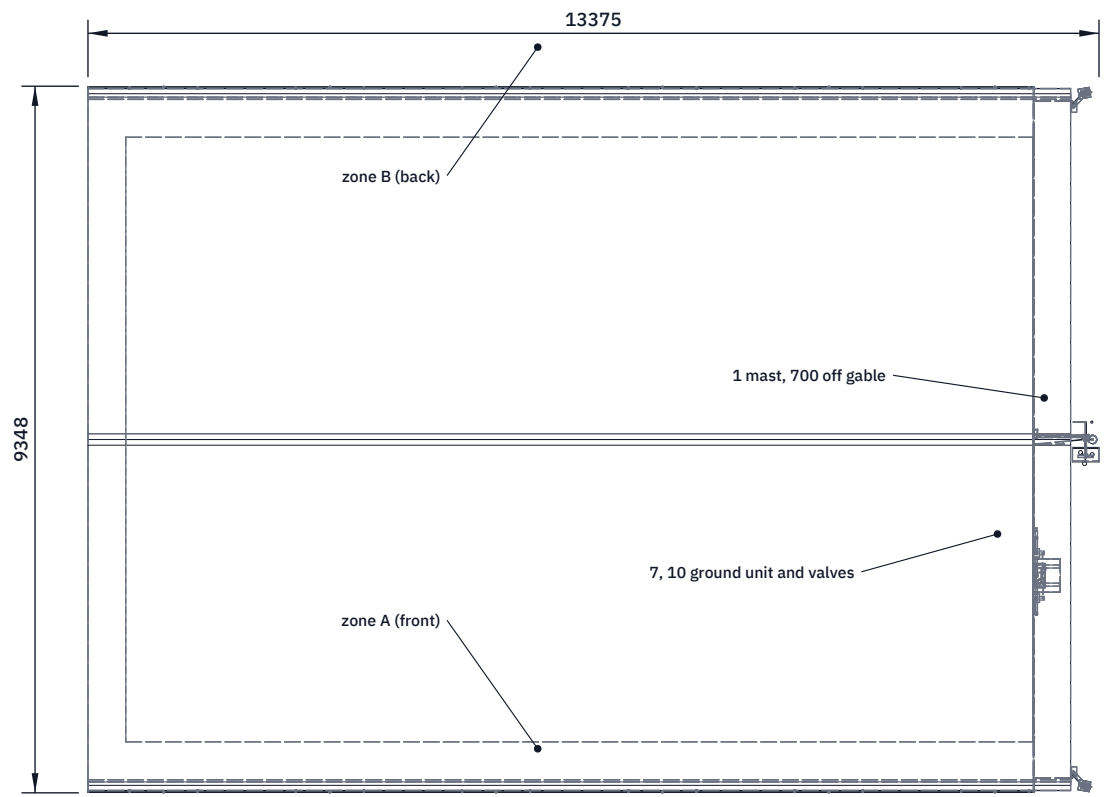


TOP VIEW

Scale 1:100; looking down (along -Z)

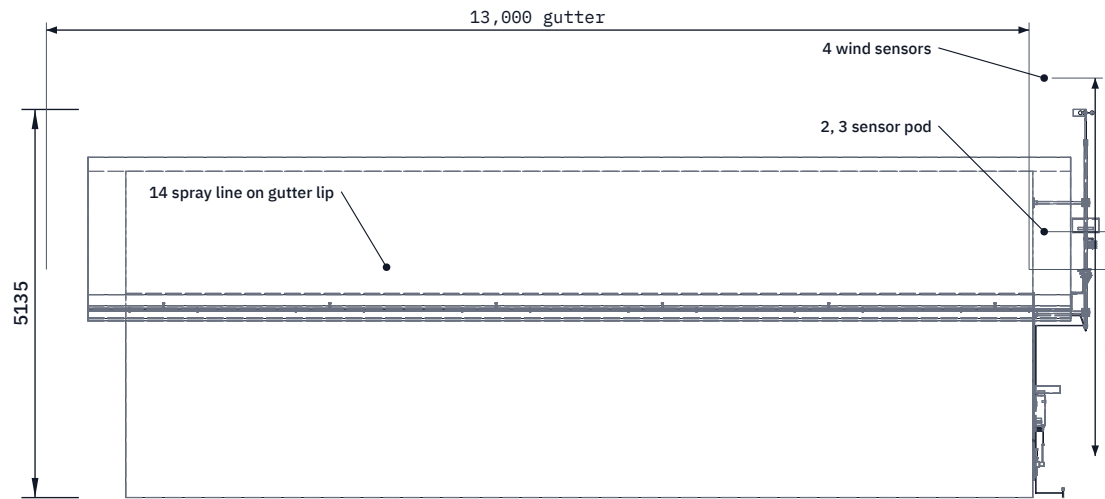

FRONT VIEW


Scale 1:100; looking at the front (along +Y)

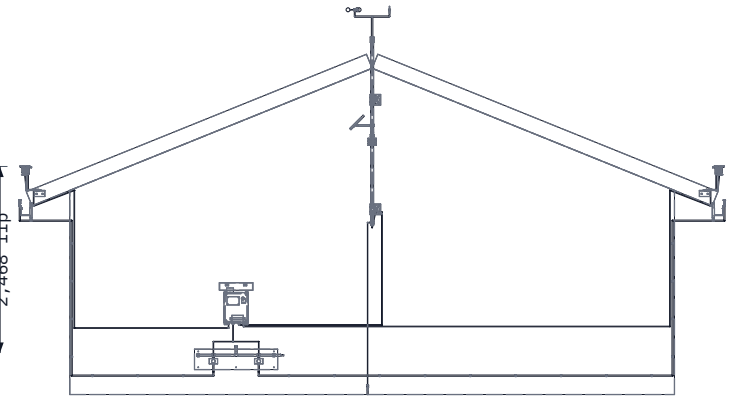

RIGHT VIEW


Scale 1:100; looking at the right side (along -X)

REV	DESCRIPTION	DATE	BY
P1	Preliminary GA for TRL 3 (from cad/src/model.py)	2026-09-25	AC
P2	Sensor pods at gutter corners, 10 Ah battery (EGD-DDR-002)	2026-09-25	AC
P3	Layout and labels tidied	2026-09-30	AC
P4	Design for construction (EGD-DDR-003)	2026-10-01	AC
P5	Sun shade over the ground enclosure (item 18) from the 2026-10-02 decisions	2026-10-02	AC

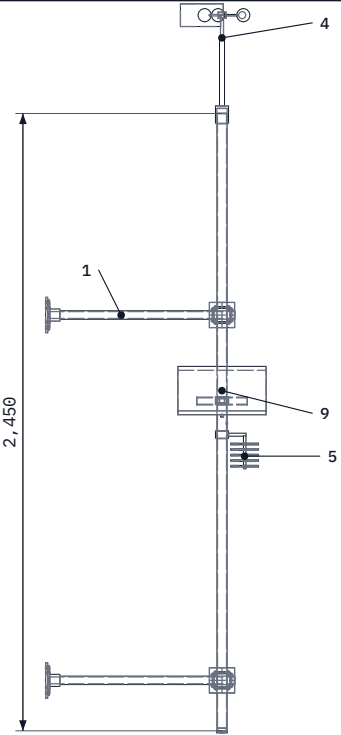

DETAIL A: MAST ASSEMBLY

Scale 1:30, from the front

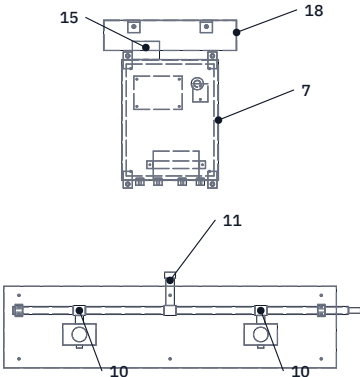

DETAIL B: GROUND UNIT

Scale 1:25, from the east

MAIN DIMENSIONS AND INTERFACES (MM)

Reference house 12,000 x 8,000, walls 2,700, roof 22 deg, eaves 500

Mast 40 x 2 Al, 2,450 long, 700 off the gable; DN25 standoffs, crossover plates

Pods 200 past each gutter end, 500 above the lip, on arms from verge cleats

Pod aim along the gutter, 10 deg in, 5 deg down

Gutter lip at 2,468; line 16 OD on lip clips, 6 heads at 2,200

Zone lines 17.5 m (A) and 21.1 m (B) incl. risers

Ground box 400 x 320 x 160 steel IP65 at 1,150, white sun shade (18) above it; valve board, manifold at 520

No roof penetrations; 12 V DC only; mast earthed (item 17)

Hanger straps shadow deep gutter debris beyond 7.8 m (EGD-CAL-001 v0.2, A4)

EMBERGUARD

github.com/BoujeeEnjinia1701/emberguard

General arrangement

DRAWING NO.

EGD-DWG-001

REV

P5

SHEET

1 of 1

SIZE

ANSI B

SCALE

1:100

UNITS

mm

PROJECTION



DATE

2026-10-02

DRAWN

Amish Chadha

MATERIAL / NOTES

House, roof, fascia and gutters are the reference house (context only); kit parts per bom/bom.csv. PRELIMINARY, NOT FOR FABRICATION

Licensed CERN-OHL-S-2.0 · Design Molecule Lab · designmolecule.com

Generated from cad/src; do not edit by hand