

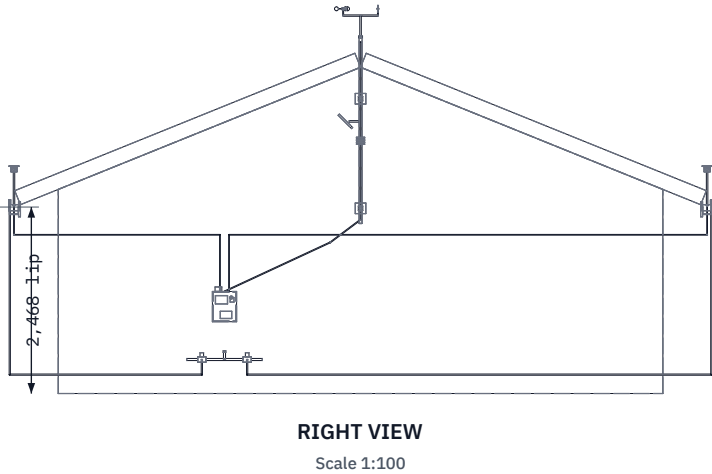
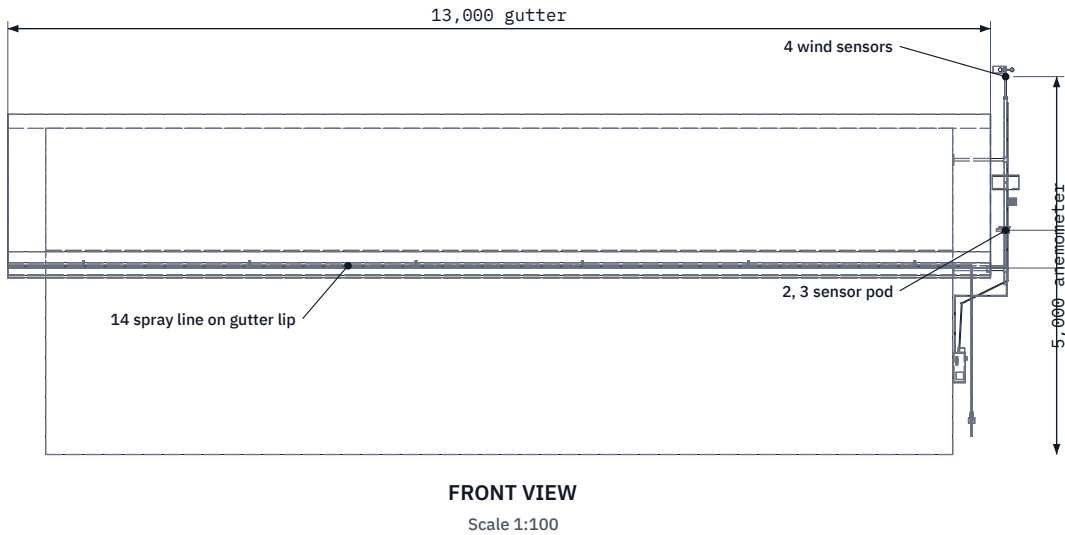
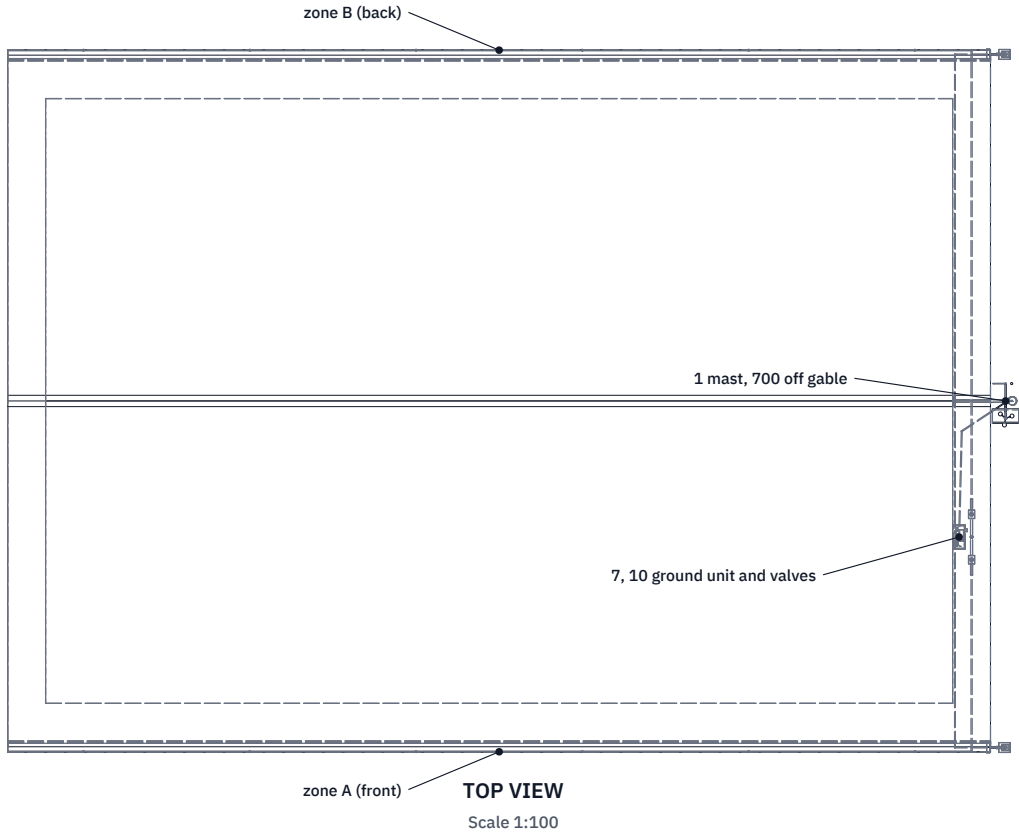


CONCEPT, NOT FOR FABRICATION

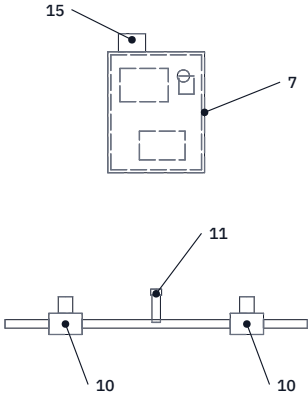

REV	DESCRIPTION	DATE	BY
P1	Preliminary GA for TRL 3 (from cad/src/model.py)	2026-09-25	AC
P2	Sensor pods at gutter corners, 10 Ah battery (EGD-DDR-002)	2026-09-25	AC

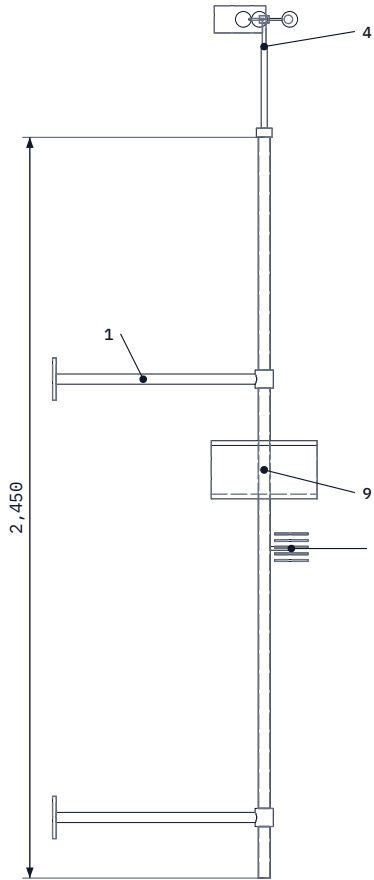

MAIN DIMENSIONS AND INTERFACES (MM)

Reference house 12,000 x 8,000, walls 2,700, roof 22 deg, eaves 500
Mast 40 x 2 Al, 2,450 long, 700 off the gable on DN25 standoffs
Sensor pods 200 beyond each gutter end, 500 above the lip; aim along the gutter, 10 deg in, 5 deg down
Gutter lip at 2,468; line 16 OD, 6 heads at 2,200 per eave
Zone lines 17.7 m (A) and 21.3 m (B) incl. risers
Ground box 400 x 320 x 160 steel IP65 at 1,150; valves at 450
No roof penetrations; 12 V DC only; mast earthed (item 17, not drawn)
Hanger straps shadow deep gutter debris beyond 7.8 m (EGD-CAL-001 v0.2, A4)

EMBERGUARD

General arrangement

DRAWING NO. EGD-DWG-001		REV P2	SHEET 1 of 1	SIZE ANSI B
SCALE 1:100	UNITS mm	PROJECTION 	DATE 2026-09-25	DRAWN Amish Chadha
MATERIAL / NOTES House, roof, fascia and gutters are the reference house (context only); kit parts per bom/bom.csv. PRELIMINARY, NOT FOR FABRICATION				
Licensed CERN-OHL-S-2.0 · Design Molecule Lab · designmolecule.com			Generated from cad/src; do not edit by hand	